B
20_02

B'

A

A'

RAMPA VEHICULAR; pend. = 10%

RAMPA VEHICULAR; pend. = 20%

ESTACIONAMIENTO SS

PLANTA SUBSUELO

esc. 1:75

B

B 20_02

IBB'

IAA'

5,0 x 2,5 m

1 2 3 4 5 6 7 8 9 10 11

28 27 26 25 24 23 22 21 20 19 18 17 16 15 14 13 12

SALA DE REUNIONES

3,64 2,10 35 3,40 2,20

13,14 2,60

1,40 1,85 1,85 1,00

2,69 1,61 1,61 1,61 1,61

50,38 5,10

1,45

ESTACIONAMIENTO PB

ÁREA TÉCNICA

RESIDUOS

GRUPO GENERADOR

ÁREA TÉCNICA TRAFO

GABINETE DE MEDICIÓN

Calle República de Colombia


PLANTA BAJA

esc. 1:75

N


B

A

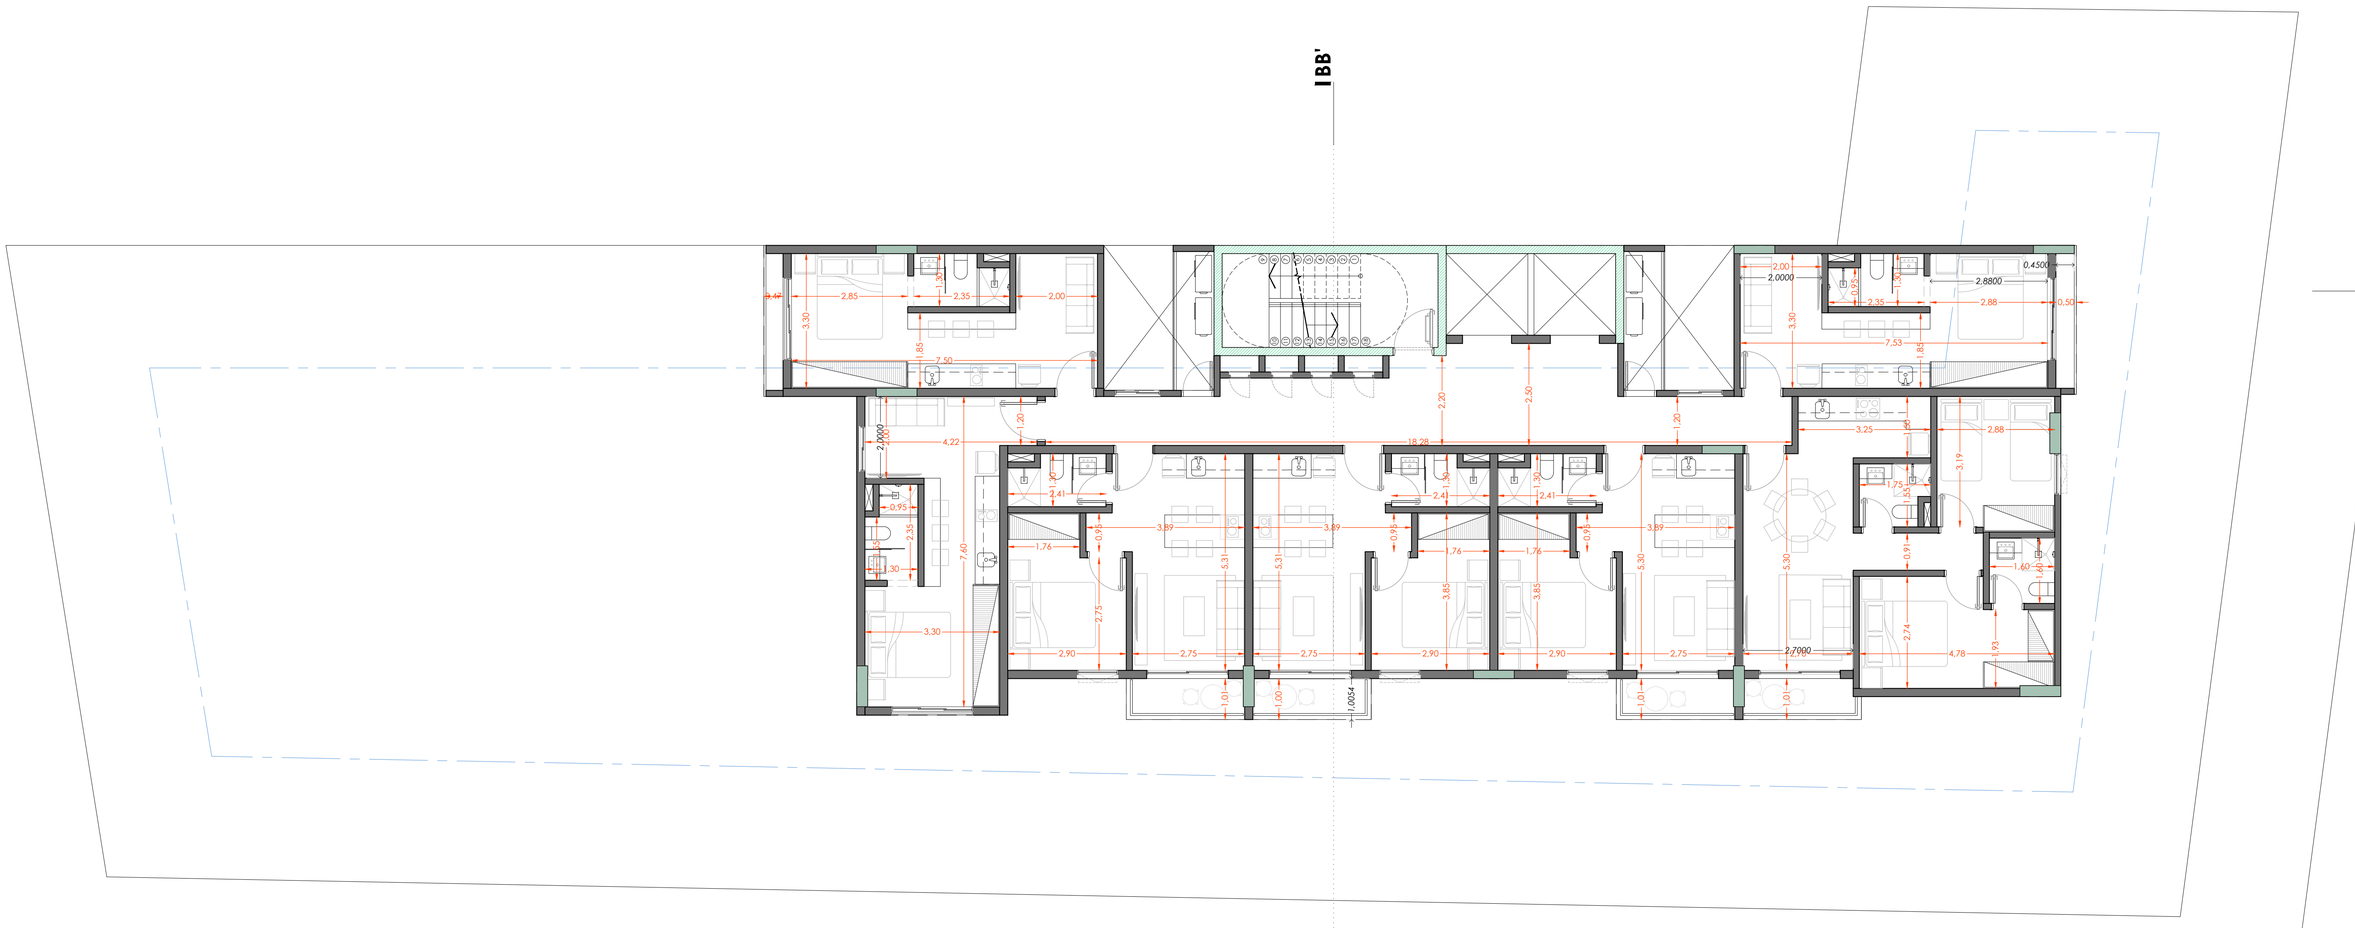


PLANTA TIPO - 1 al 14

esc. 1:75

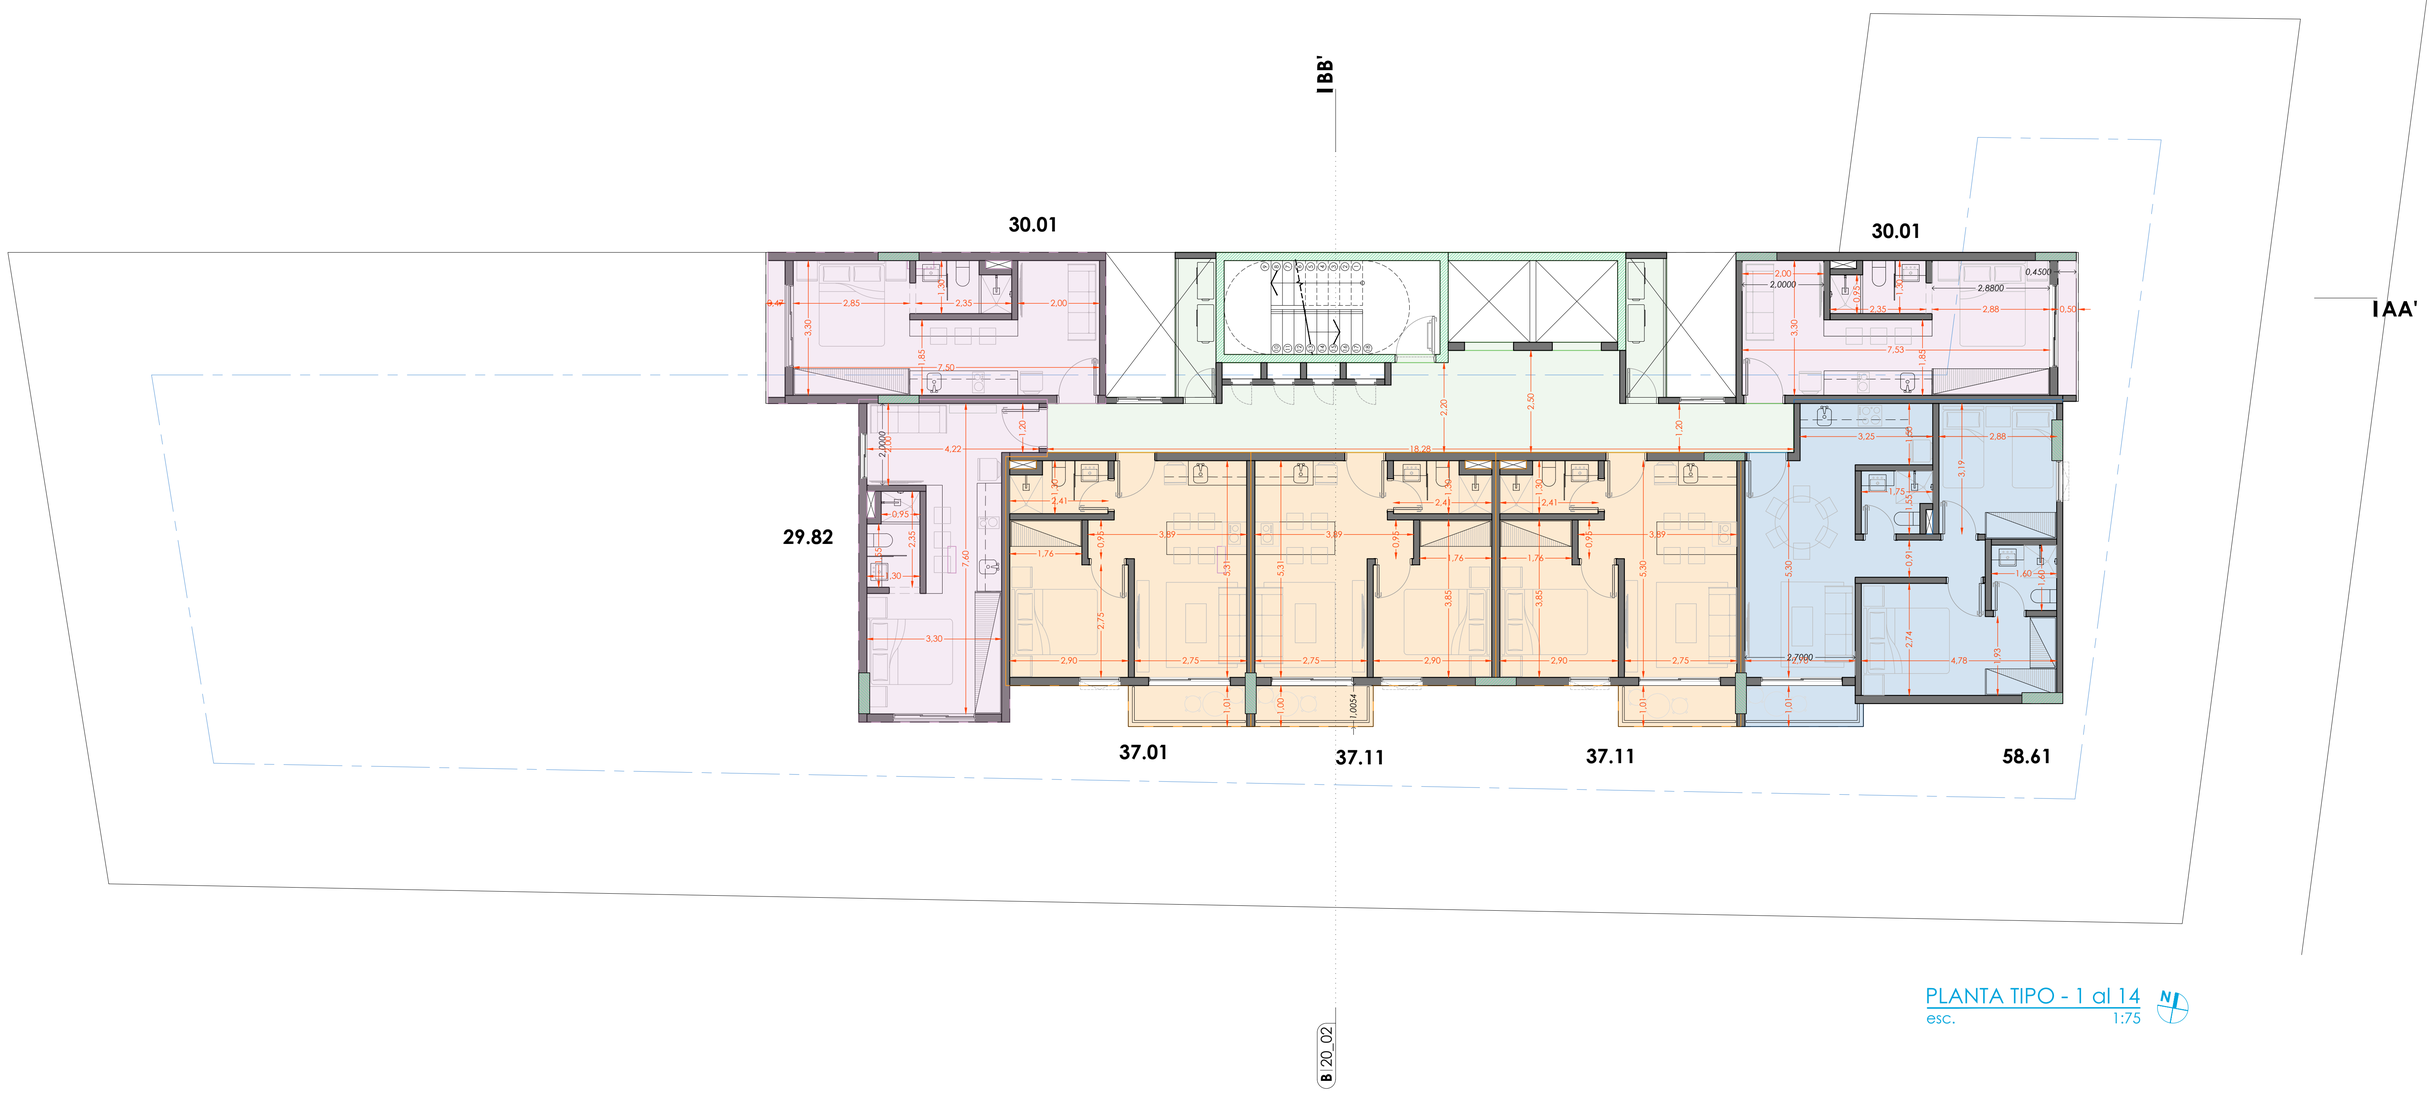

PLANTA TIPO - 1 al 14

esc. 1:75

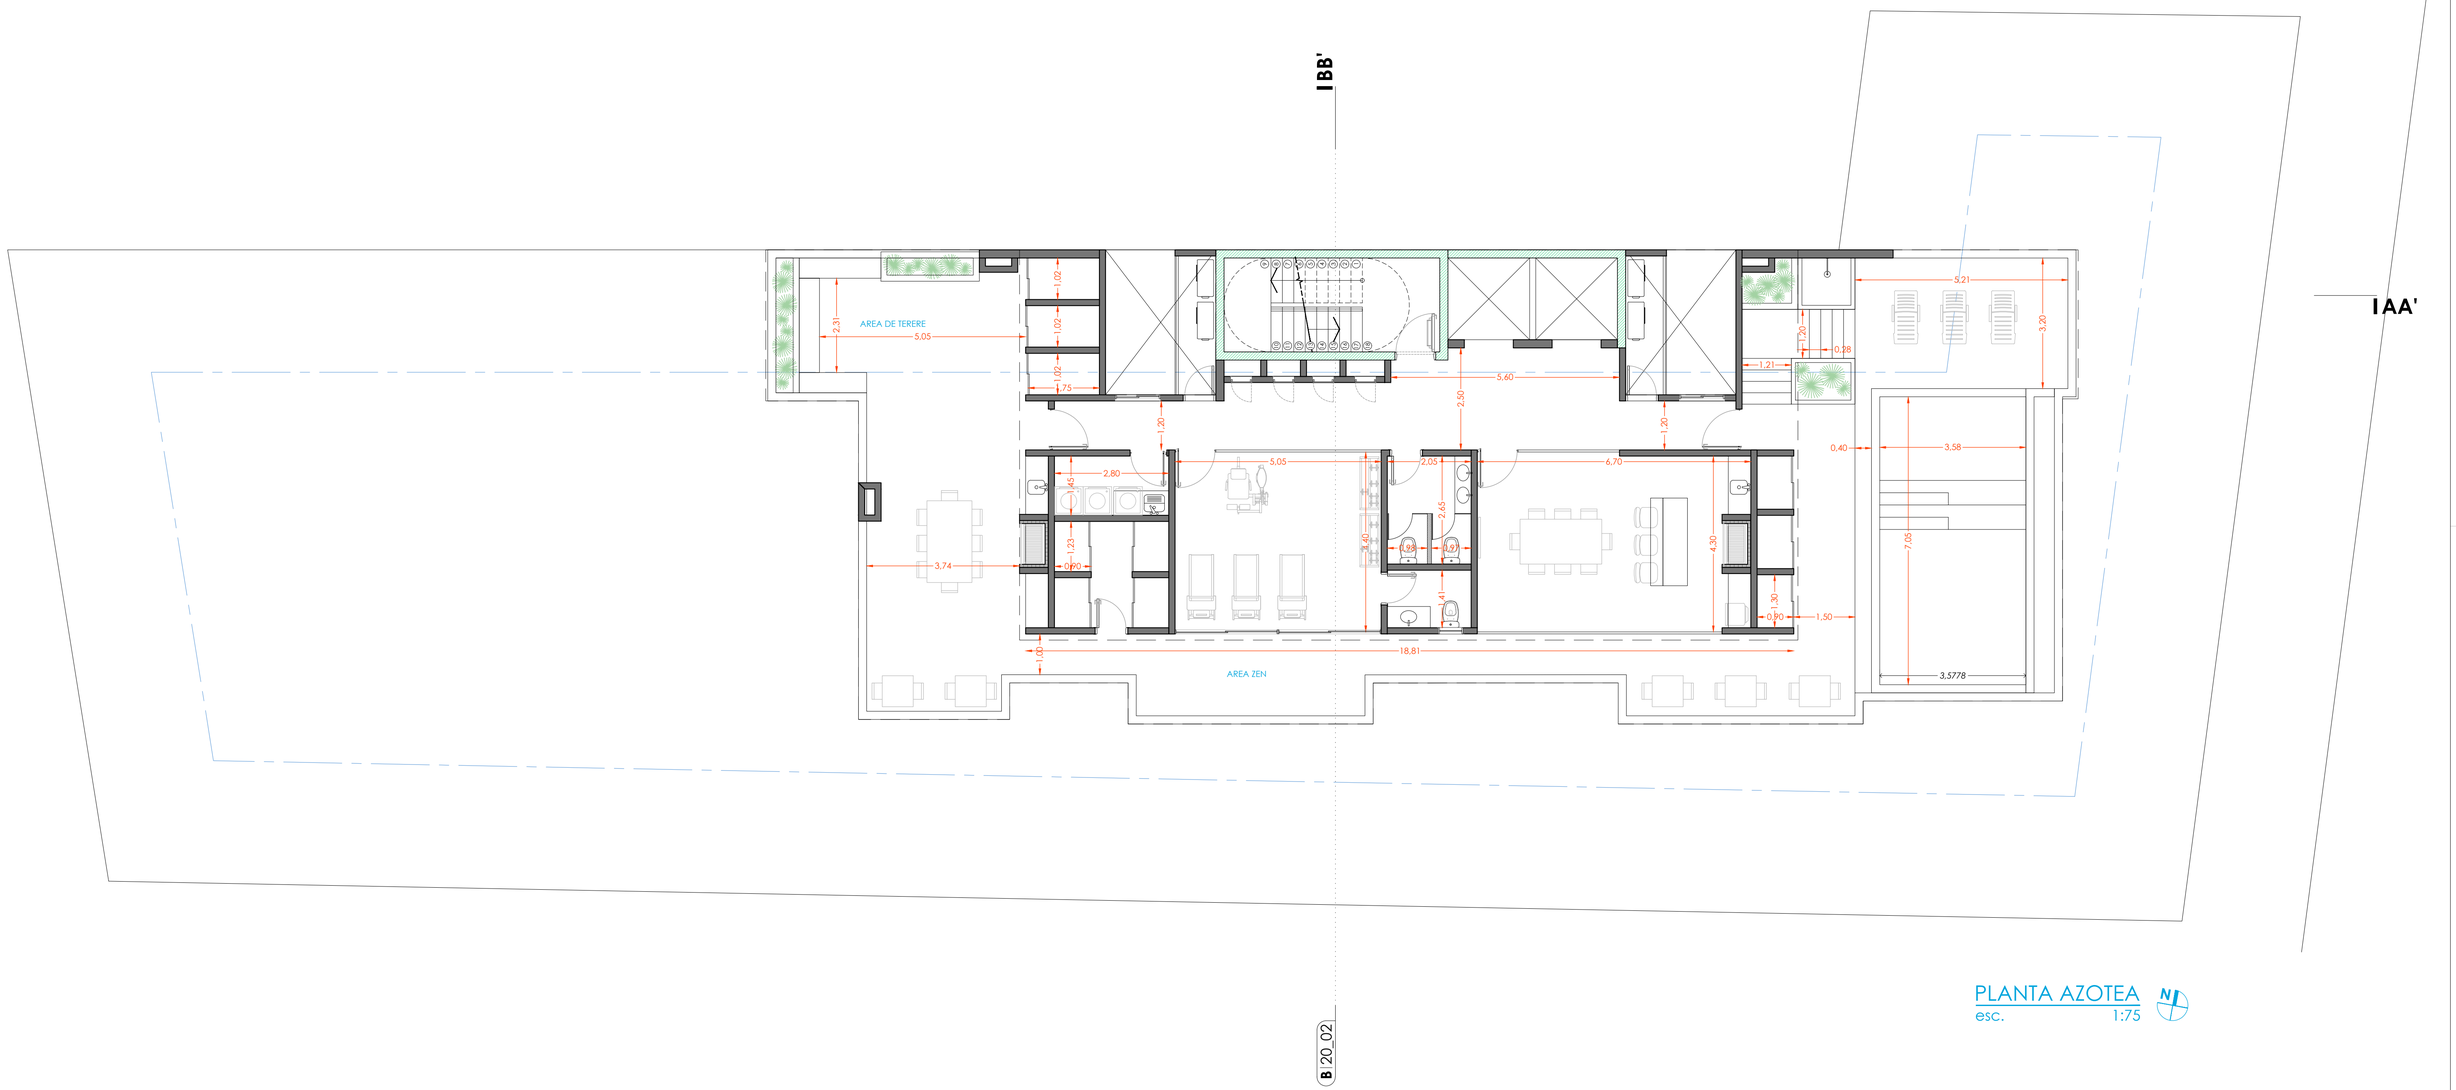

PLANTA AZOTEA

esc. 1:75

B 20_02